


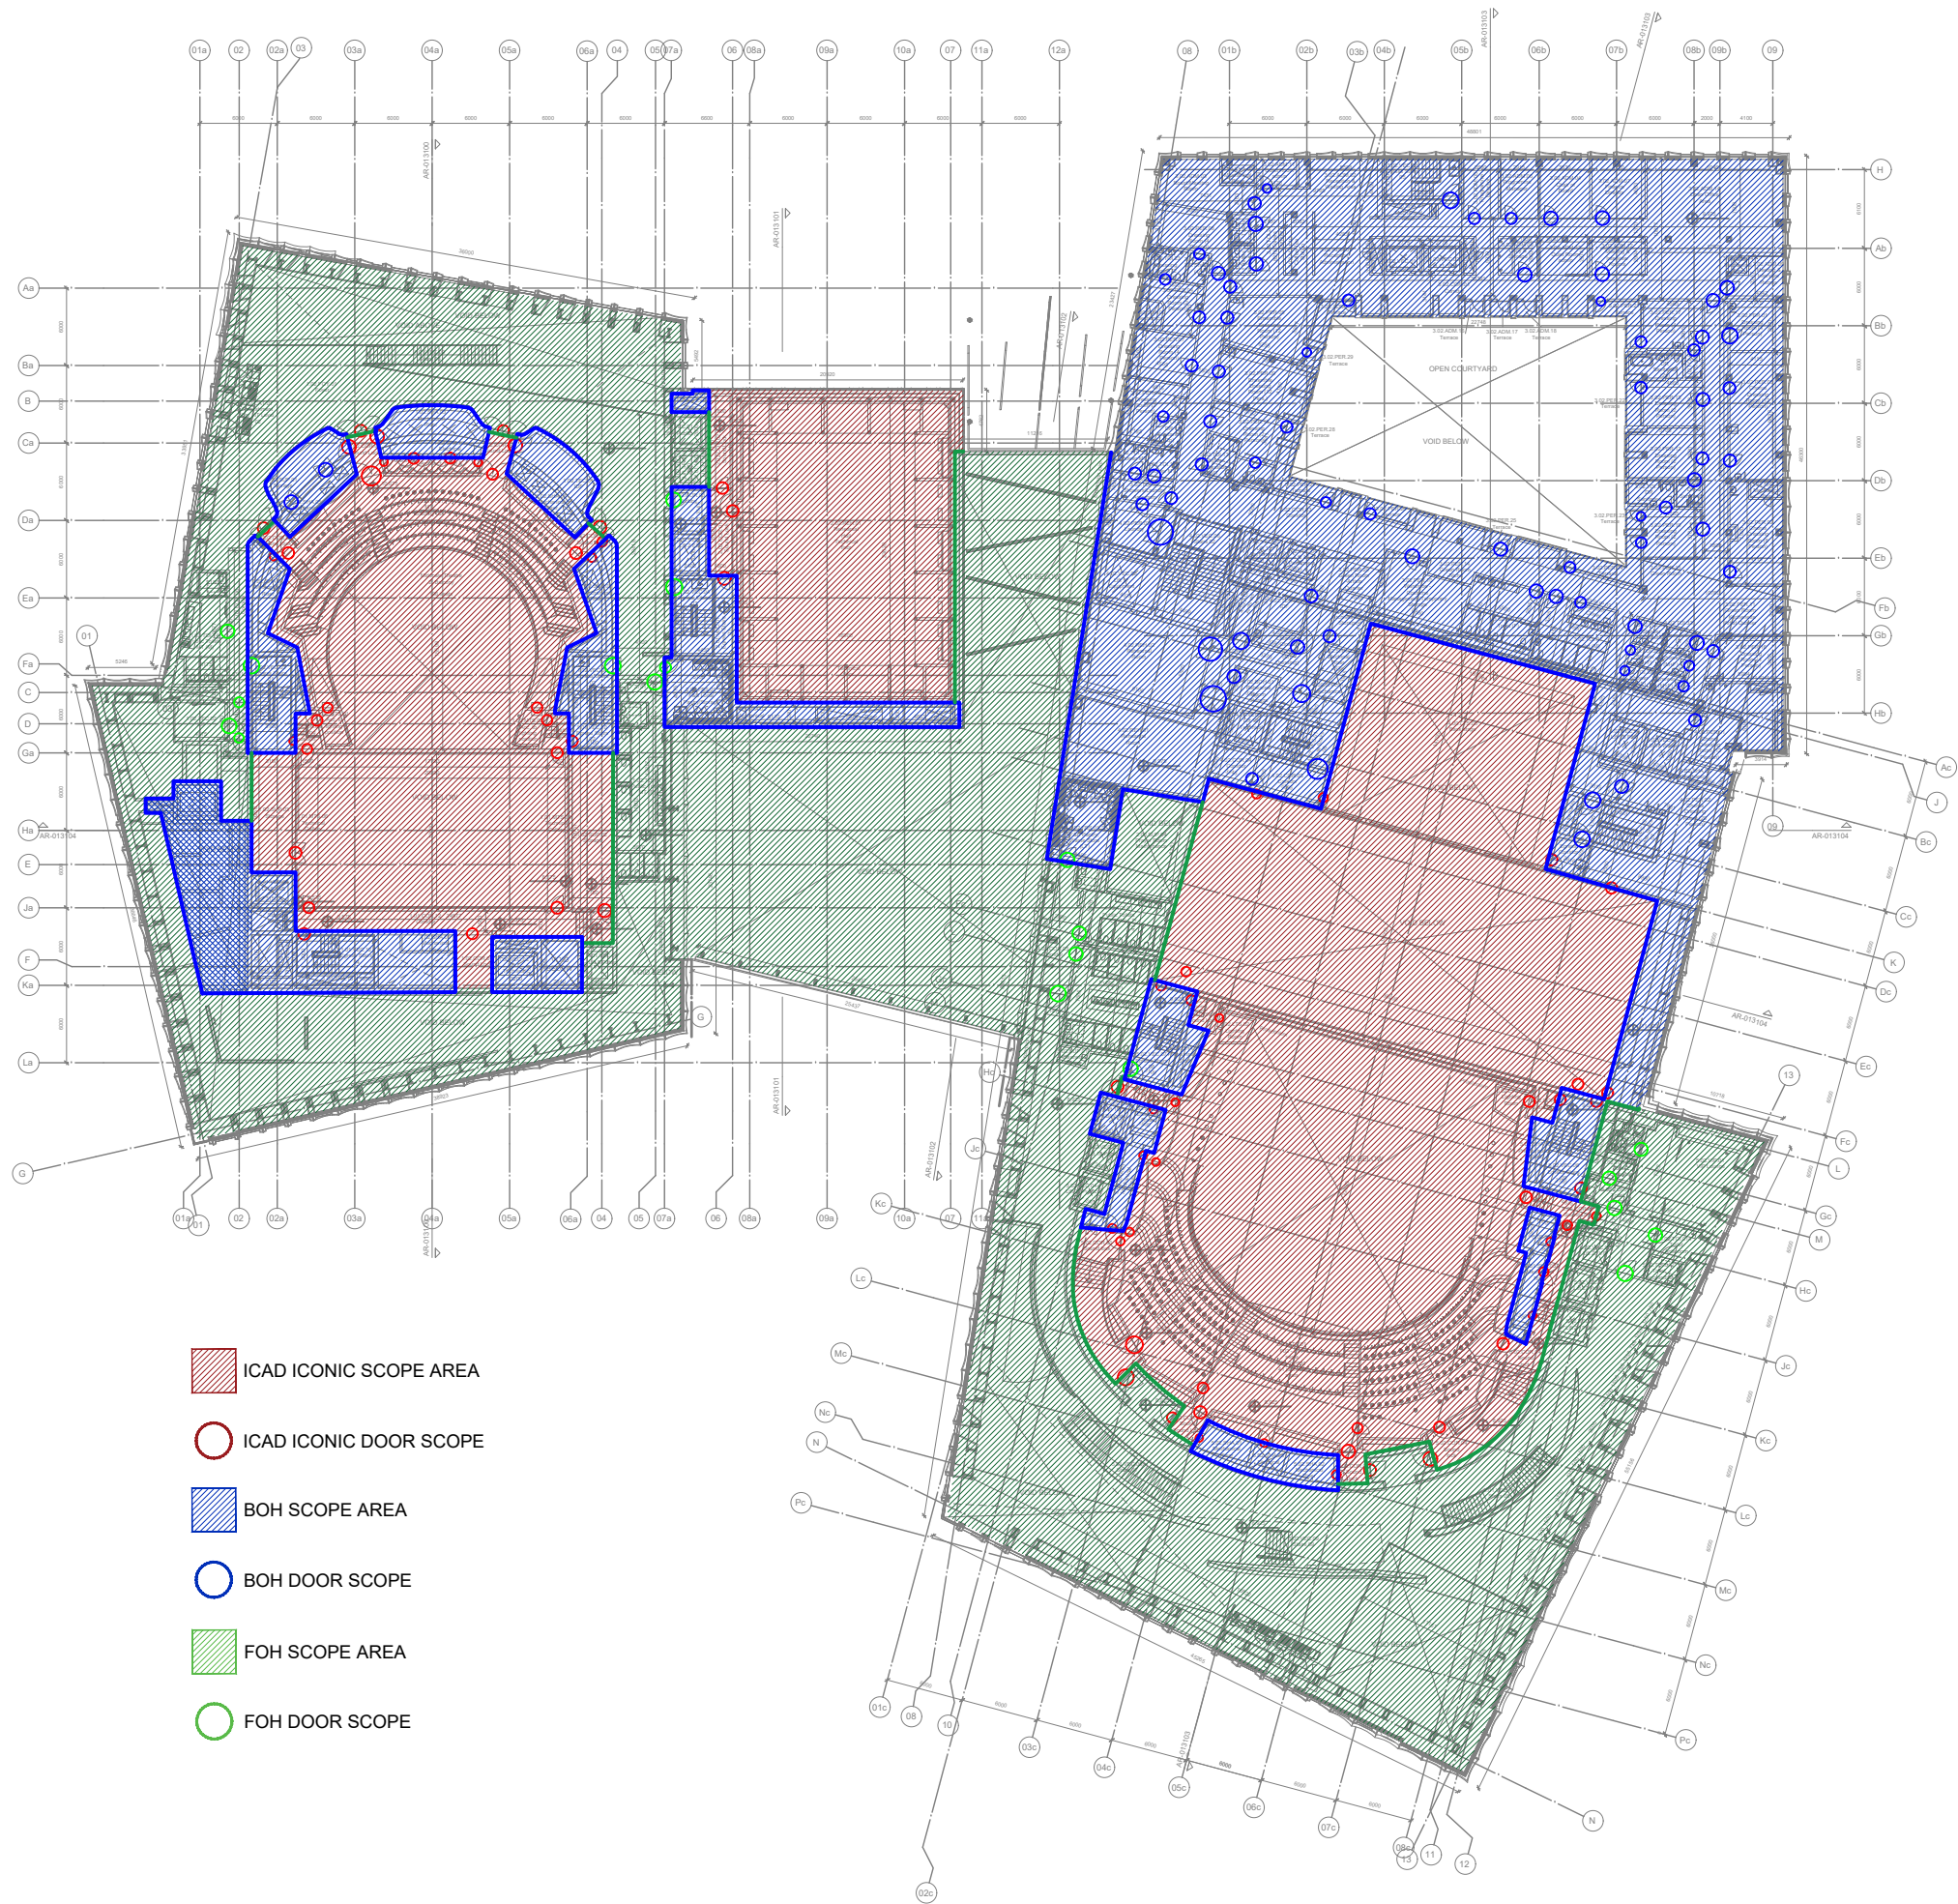

- ICAD ICONIC SCOPE AREA
- ICAD ICONIC DOOR SCOPE
- BOH SCOPE AREA
- BOH DOOR SCOPE
- FOH SCOPE AREA
- FOH DOOR SCOPE

INDEX PLAN

BUILDING KEY PLAN

GENERAL NOTES

LEGEND & ABBREVIATIONS

REV	DATE	BY	REASON FOR CONSTRUCTION	CHK	APR
F00	31-01-2024	DR	Issued for Construction	LFN	MF

Issued for Construction

CLIENT

LEAD DESIGN CONSULTANT

LEAD ENGINEERING CONSULTANT

GENERAL CONTRACTOR

GENERAL CONTRACTOR

PROJECT

JEDDAH OPERA HOUSE

TITLE

ARCHITECT
PLAN
LEVEL 02

SCALE AS SHOWN	CHECKED LFN	APPROVED MF	MODEL FILE REF
1:200	LFN	MF	JOH-HLA-S4-01-056-XXX-02-DR-AR-011120

PROJECT NO.	DESIGNED	DRAWN	CHECKED
198020123	HLA	VCS	31-01-2024

DRAWING NO.

JOH-HLA-S4-01-056-XXX-02-DR-AR-011120

REV

F00

©JCDC