


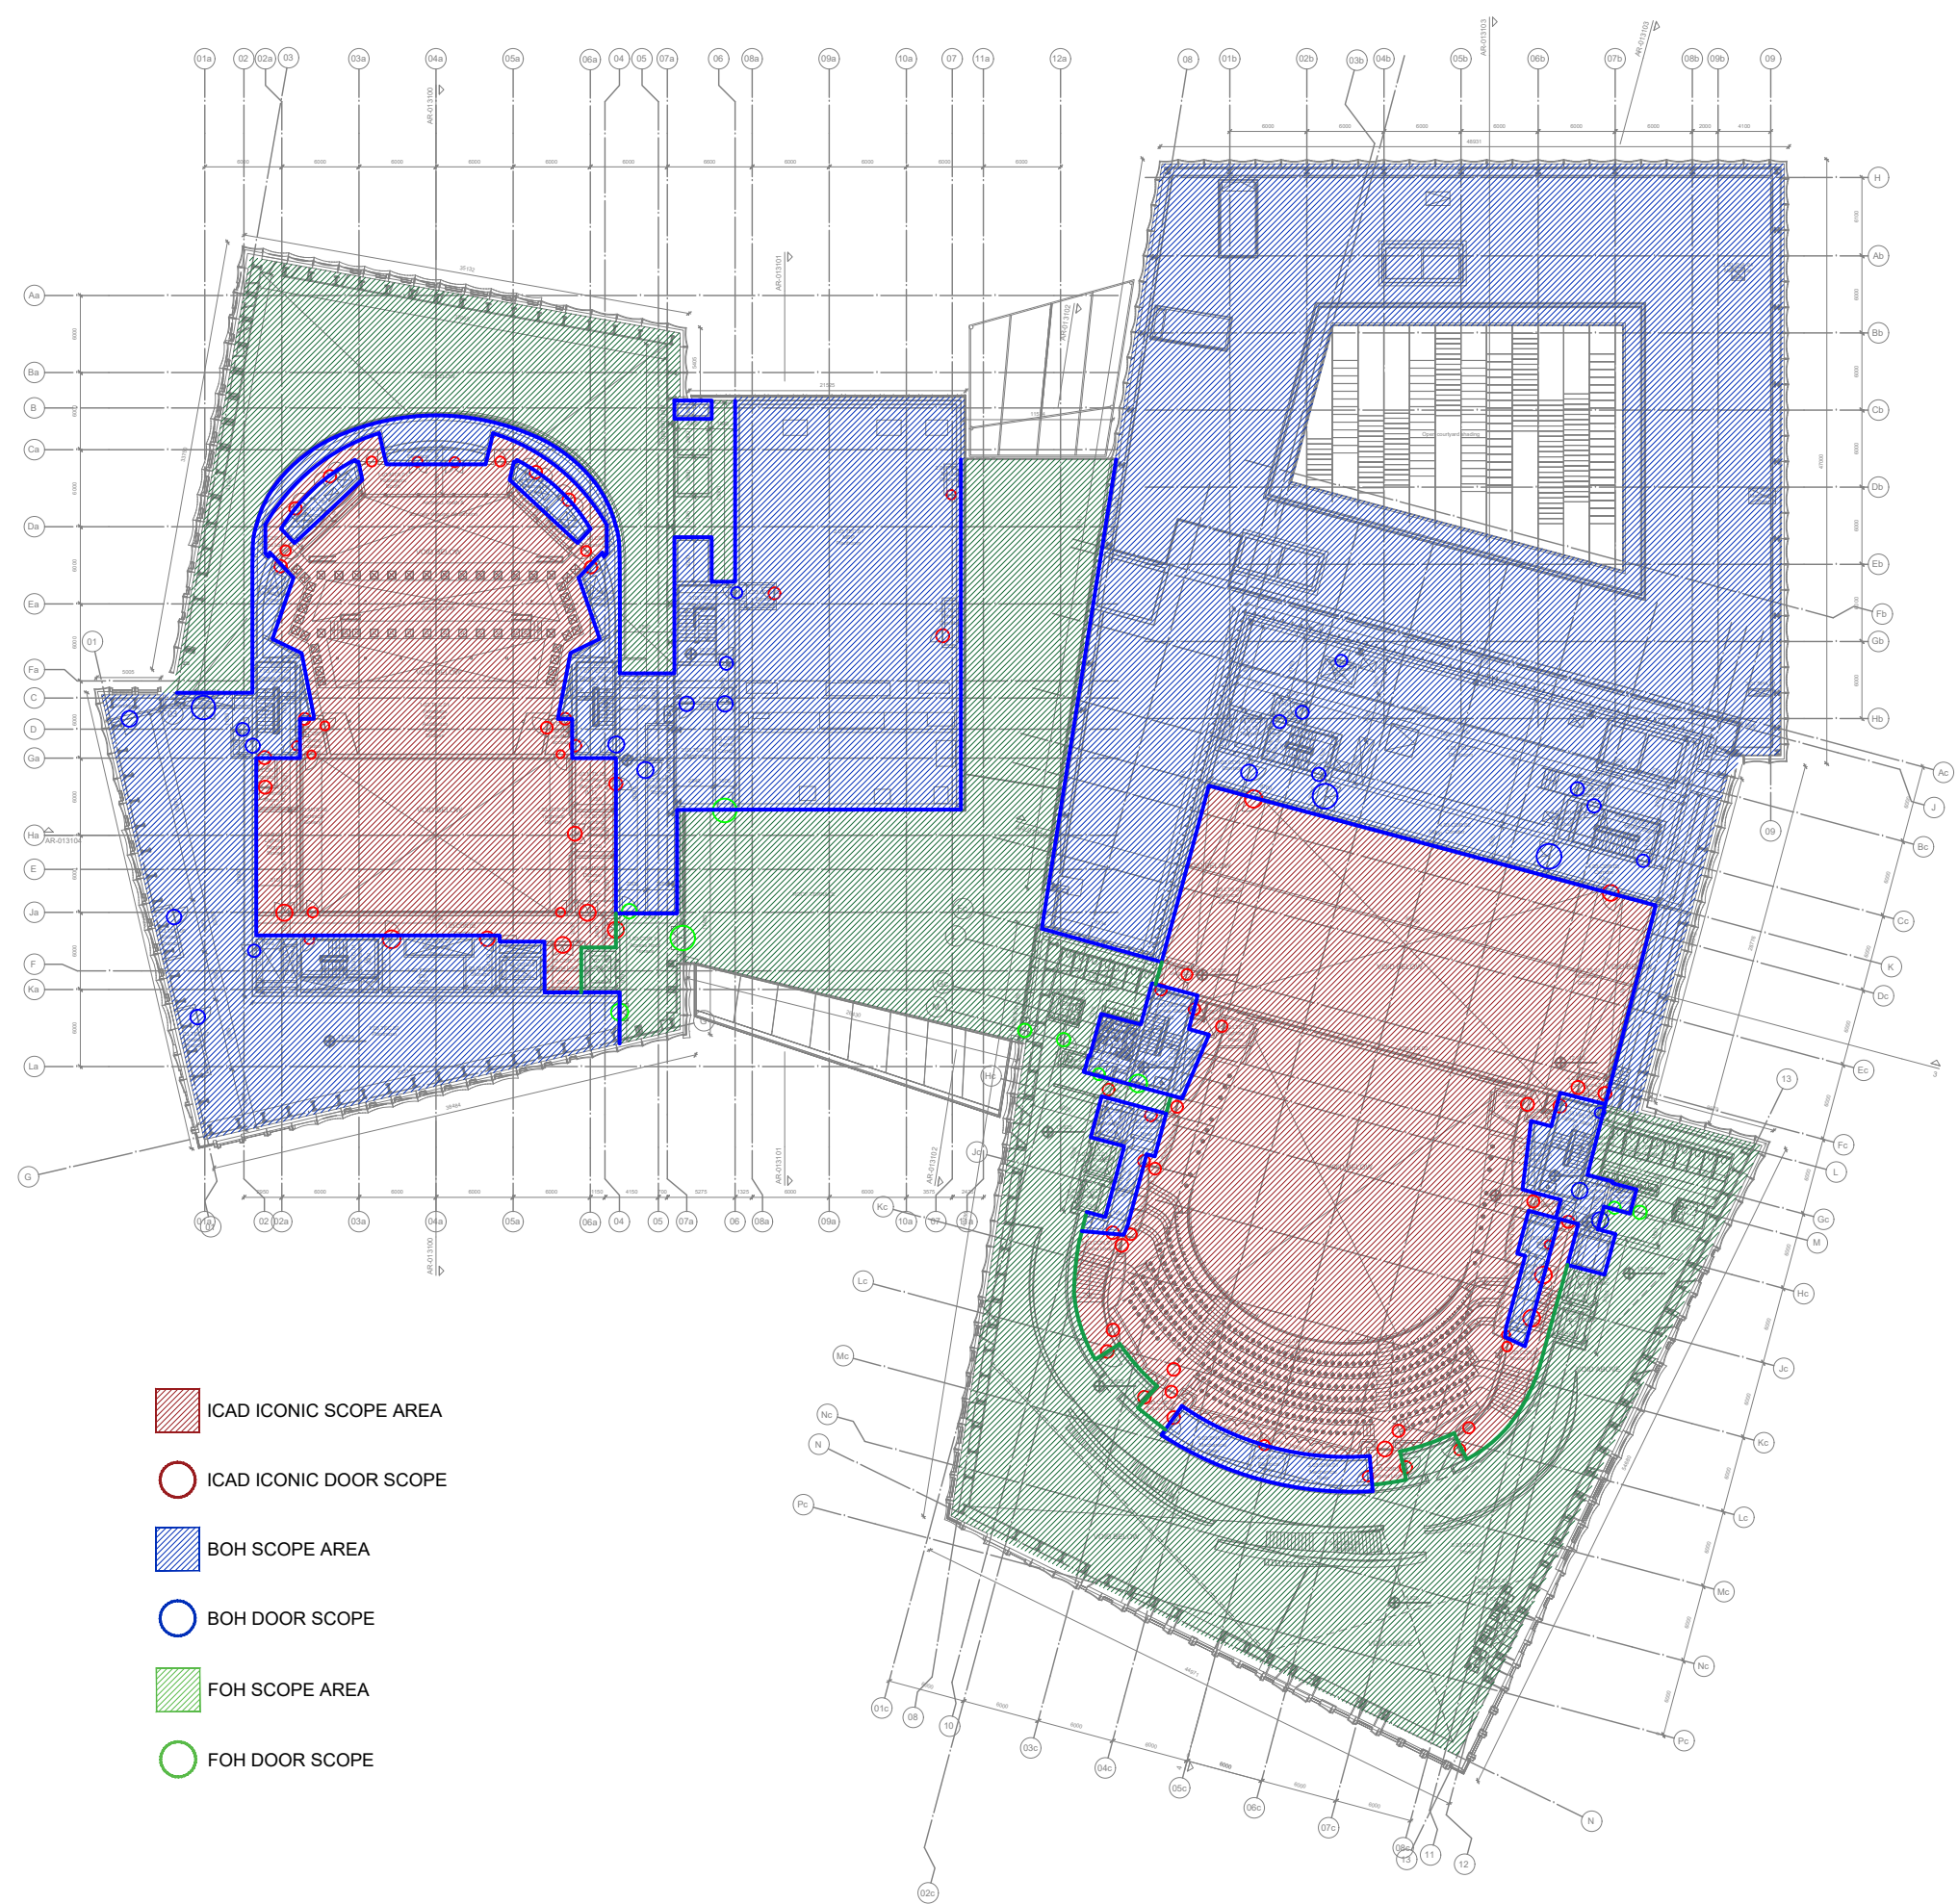

- ICAD ICONIC SCOPE AREA
- ICAD ICONIC DOOR SCOPE
- BOH SCOPE AREA
- BOH DOOR SCOPE
- FOH SCOPE AREA
- FOH DOOR SCOPE

DO NOT SCALE

INDEX PLAN

BUILDING KEY PLAN

GENERAL NOTES

LEGEND & ABBREVIATIONS

REV	DATE	BY	DESCRIPTION	CHK	APR
F00	31-01-2024	DR	Issued for Construction	LFN	NF

Issued for Construction

CLIENT

LEAD DESIGN CONSULTANTS

LEAD ENGINEERING CONSULTANT

GENERAL CONTRACTOR

PROJECT

FILE

ARCHITECT
PLAN
LEVEL 03

SCALE AS SHOWN	CHECKED	APPROVED	MODEL FILE REF
1:200	LFN	NF	JOH-HLA-S4-01-056-XXX-03-DR-AR-011130

PROJECT NO.	DESIGNED	DRAWN	DATE
1980020123	HLA	VCS	31-01-2024

DRAWING NO.	REV
JOH-HLA-S4-01-056-XXX-03-DR-AR-011130	F00

©JCDC