


INDEX PLAN

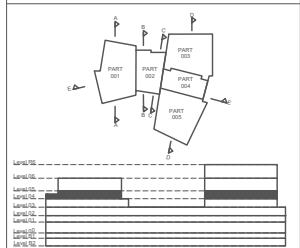

BUILDING KEY PLAN

GENERAL NOTES

1. The line serves as an indicative guide, and the partial plans should be used for accurately establishing the joint line in the finishes.

ISSUES & APPROVALS

Interior Joint Details:
- JCH-HLA-S4-01-056-XXX-ZZ-DR-AR-015800
See facade detail package for exterior joints

REV	DATE	BY	DESCRIPTION	CHK	APR
F00	31-01-2024	DR	Issued for Construction	LFN	NSF

DRAWING STATUS: Issued for Construction

CLIENT:

© 2024 JCH-HLA-S4-01-056-XXX-ZZ-DR-AR-015800

LEAD DESIGN CONSULTANTS

LEAD ENGINEERING CONSULTANT

GENERAL CONTRACTOR: GENERAL CONTRACTOR

PROJECT: JEDDAH OPERA HOUSE


TITLE: ARCHITECT PLAN LEVEL 04

SCALE AS SHOWN	CHECKED LFN	APPROVED NSF	MODEL FILE REF
1:200	HLA	VCS	JCH-HLA-S4-01-056-XXX-ZZ-DR-AR-015800

PROJECT NO.	DATE	REV.
198020123	31-01-2024	F00

DRAWING NO.: JCH-HLA-S4-01-056-XXX-04-DR-AR-011140

©JCDC

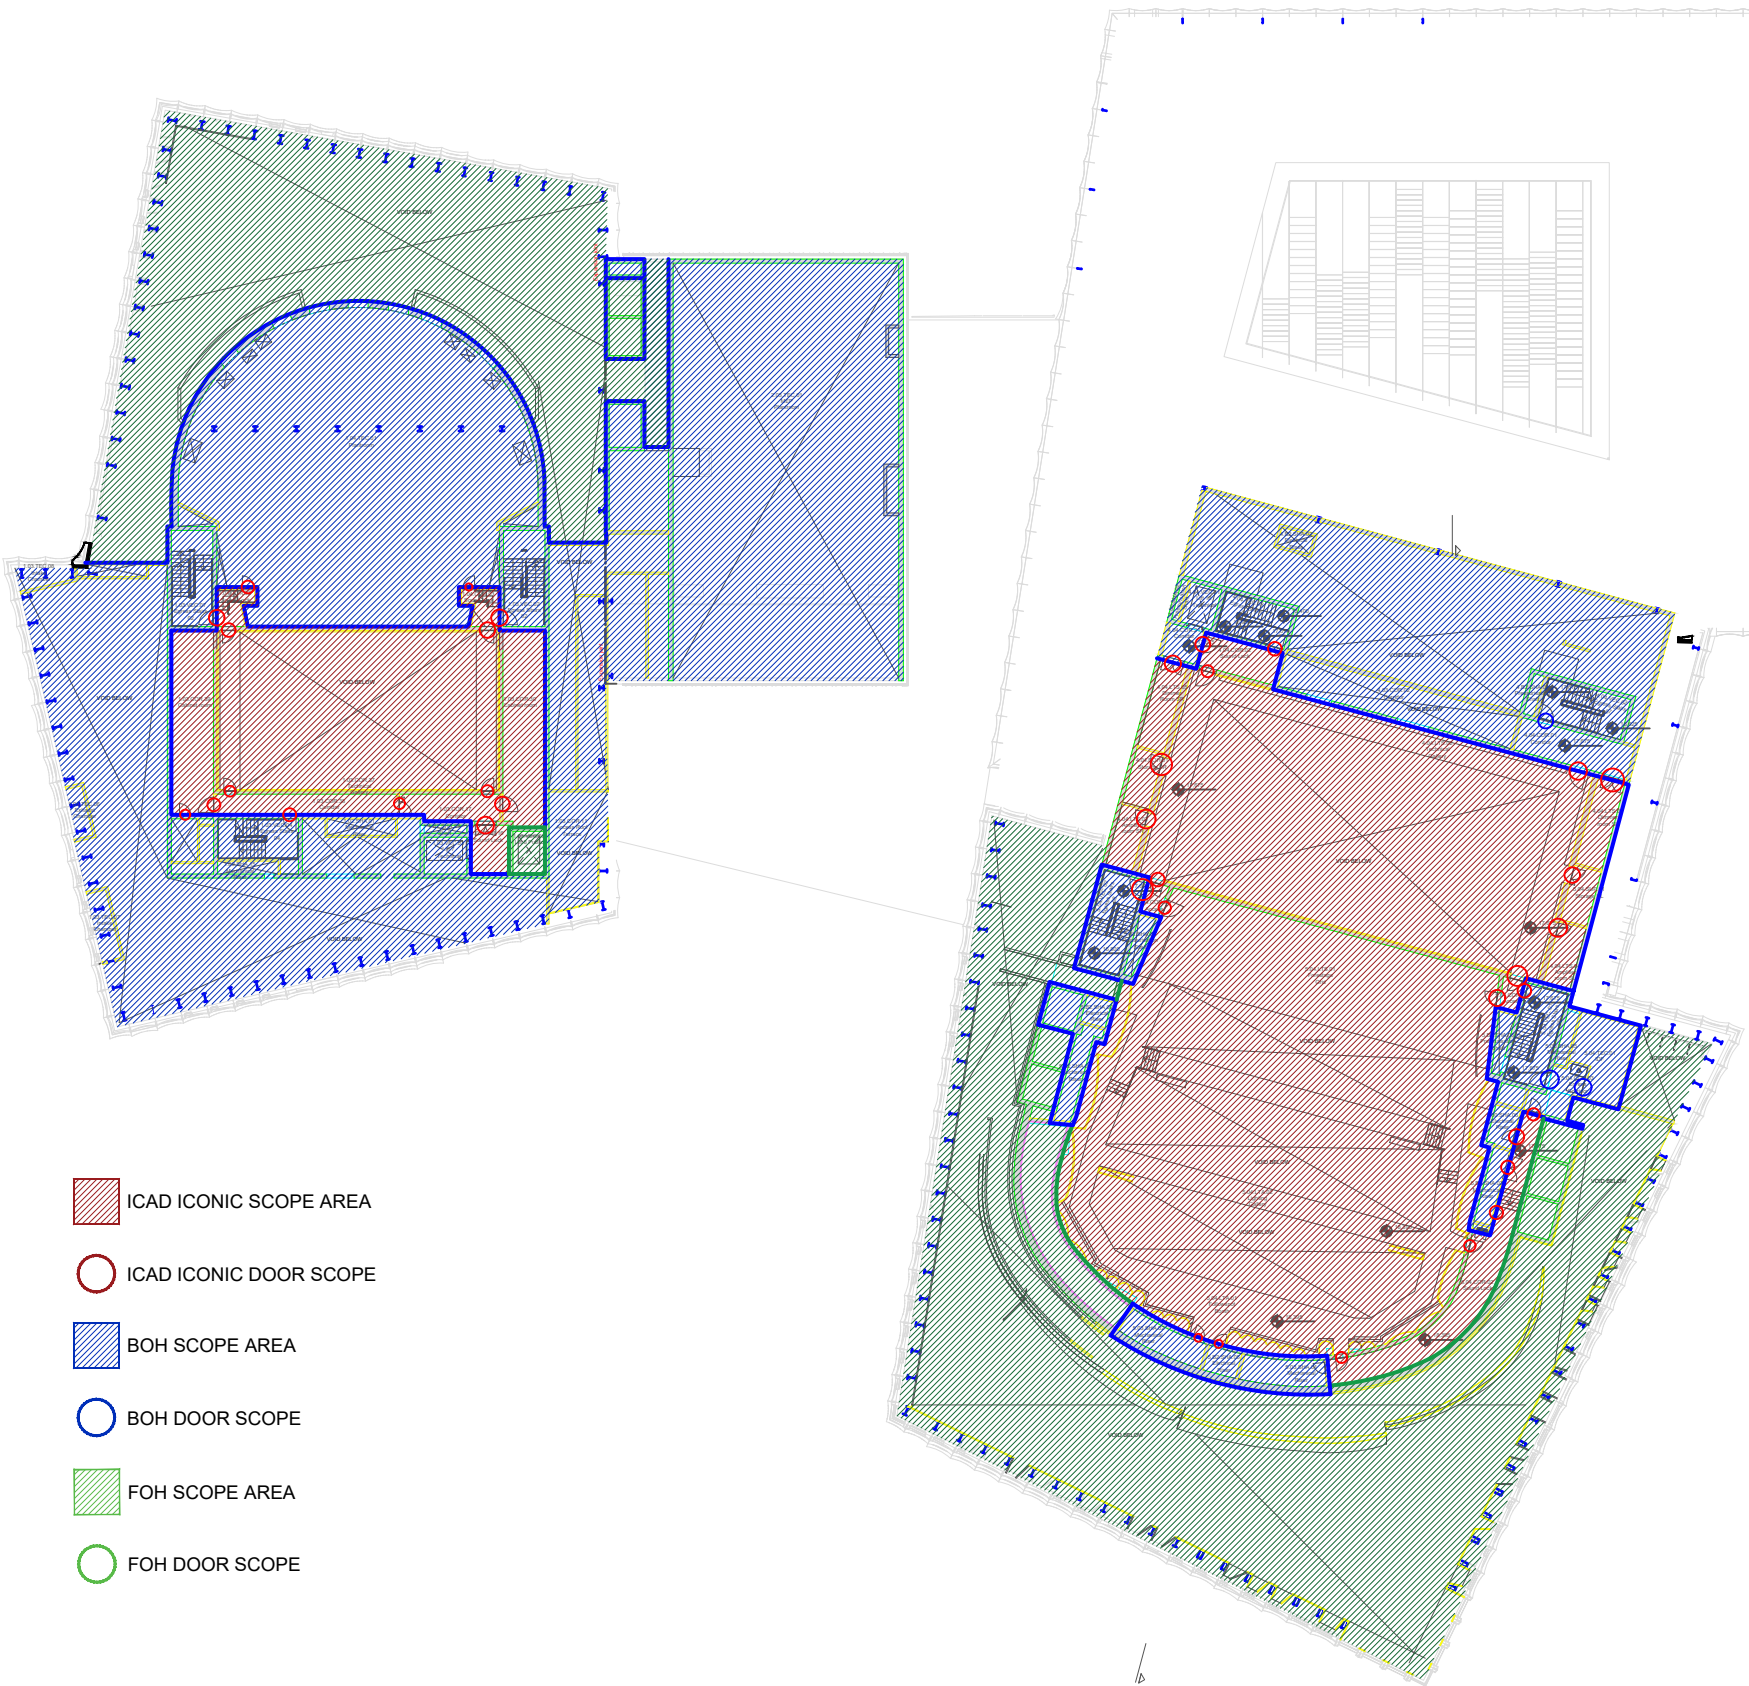

- ICAD ICONIC SCOPE AREA
- ICAD ICONIC DOOR SCOPE
- BOH SCOPE AREA
- BOH DOOR SCOPE
- FOH SCOPE AREA
- FOH DOOR SCOPE